

MIRANDA
MORTON

PORTFOLIO

PROFILE



MIRANDA MORTON

Architectural designer with an M.Arch and nearly four years of experience in multifamily housing, including market-rate, student, and affordable senior projects. Hands-on across all project phases (SD, DD, CD, CA), with strengths in technical documentation, Revit production, and consultant coordination. NCARB record established with active AXP hours.

📞 (510)673-8785
✉ mirandamorton7@yahoo.com
🌐 miranda-morton.com
📍 Miami, FL

EXPERIENCE

- Sept 2022 - May 2026 **JLA Architects** — Architectural Intern (part time, concurrent with degrees)
- All phases: SD, DD, CD, CA
 - Market-rate, student, and affordable senior housing
 - Master plan for The Hangar at Central Park
 - Contributed to 112/146 CD sheets
 - Design Charrette for Ravenfield
 - Client and consultant coordination
- Jun 2025 - May 2026 **The Mulhern Group** — Admin Assistant & Studio Floater (part time)
- Redline pickups and drawing revisions
 - AR/AP processing, expense filing, cash flow logs
- Aug 2018 - Jul 2022 **Waterworks Aquatics** — Senior Lead Instructor (part time)
- Swim instruction, ages 3+
 - Mentored junior instructors
 - CPR, AED, First Aid certified

EDUCATION

- Aug 2022 - May 2026 **University of Colorado Denver**
- M.Arch
 - BS Architecture
- Aug 2018 - May 2022 **Chabot College**
- AA & AS Architecture

LICENSURE

NCARB record established; actively logging AXP experience hours

SKILLS



CONTENTS

01 THE HANGAR AT CENTRAL PARK



JLA ARCHITECTS

02 THE HANGAR AT CENTRAL PARK




JLA ARCHITECTS

03 RAVENFIELD



JLA ARCHITECTS

04 MASTER PLANS

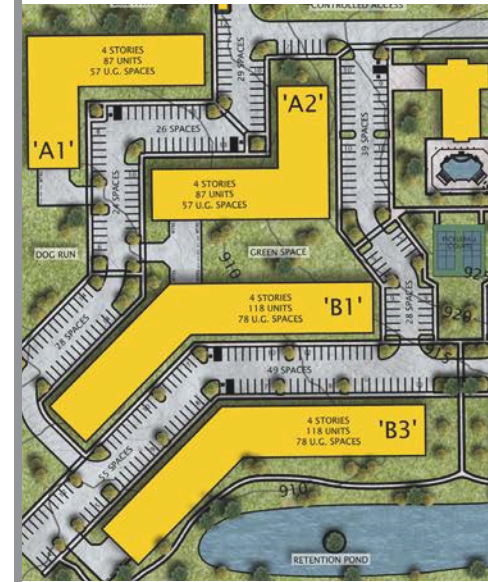

JLA ARCHITECTS

05 MUSEUM OF NATIVE AMERICAN ART




M ARCH

06 MODEST MONUMENTALITY



M ARCH

07 TECHNICAL SKETCHING

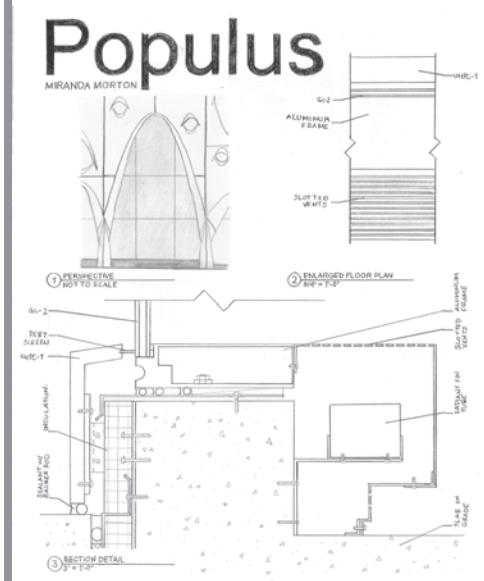

M ARCH

08 COMMONS PARK








BS ARCH

01 | THE HANGAR

INDEPENDENT WORK






JLA ARCHITECTS HANGAR AT CENTRAL PARK
RENDERED MASTERPLAN
MAY 24, 2023
1" = 80'

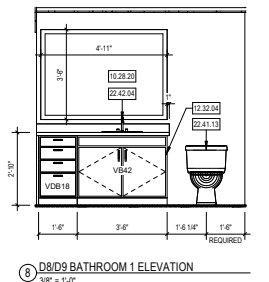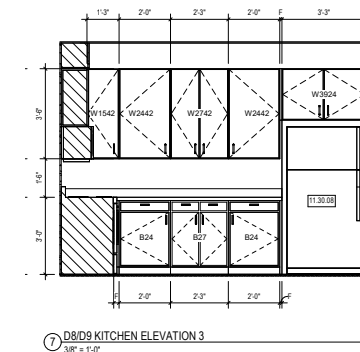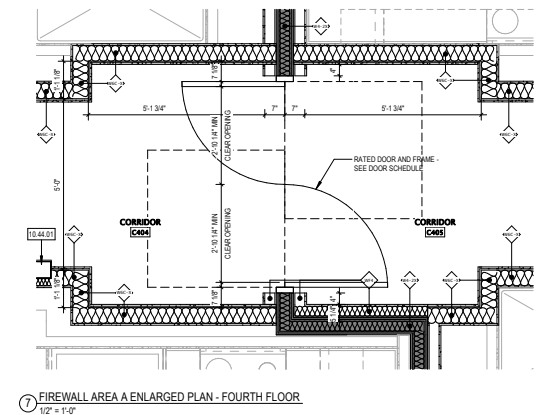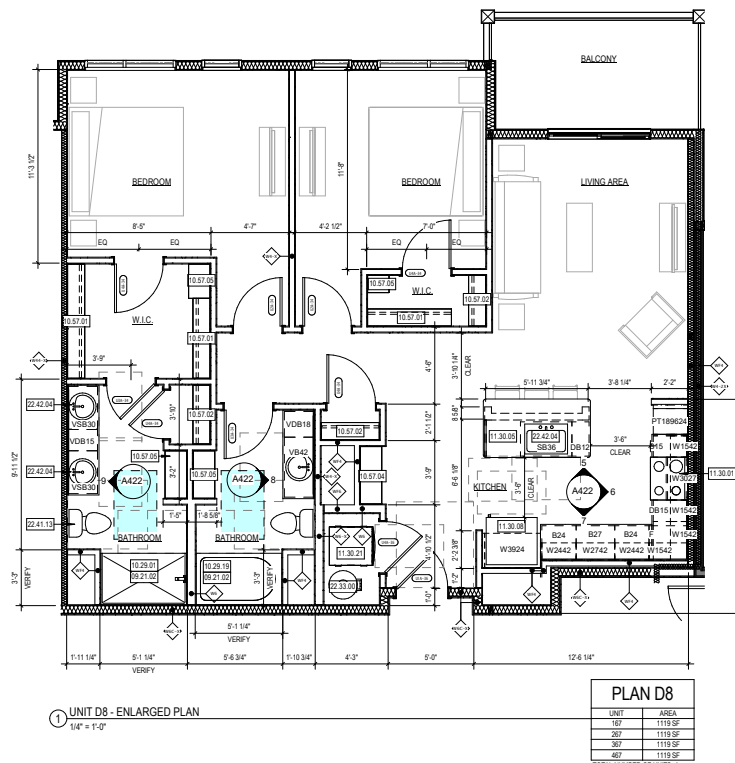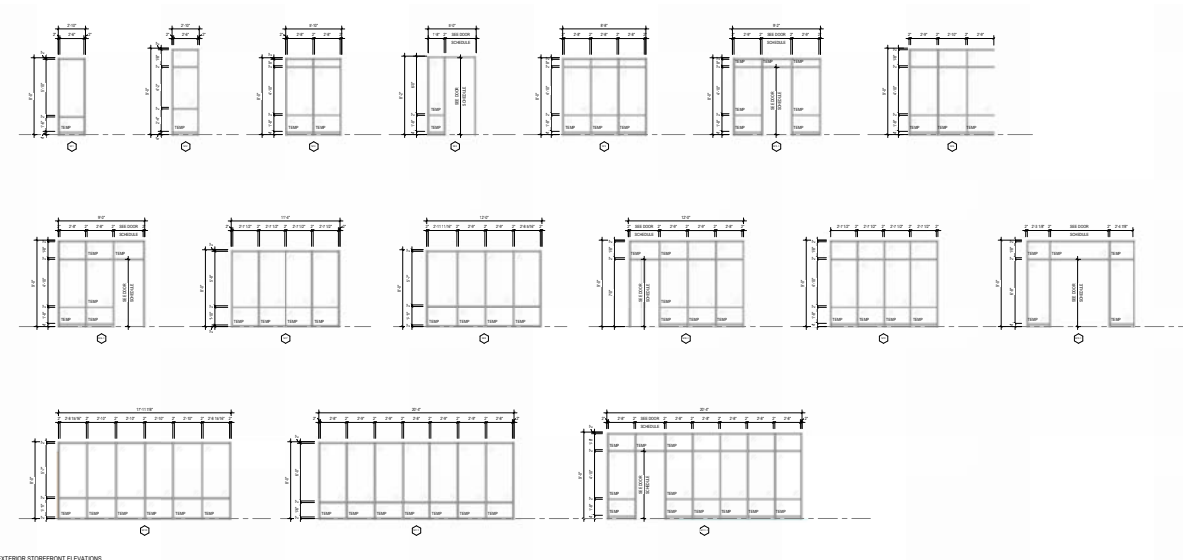

A 4-story, 259-unit multifamily project by JLA Architects located in Denver's Central Park neighborhood. Shown are sheets independently produced as part of the construction document set: firewall plans, enlarged unit plans, interior elevations, and storefront framing elevations, as well as the independently produced master plan.



Type: Multifamily
Location: 8399 E 23rd, Denver, CO
Completion Date: Spring 2028
Client: Clear Sky Capital
Units: 259
Construction Cost: \$63 million
Programs: Revit, AutoCAD, Photoshop

02 | THE HANGAR TEAM CONTRIBUTIONS

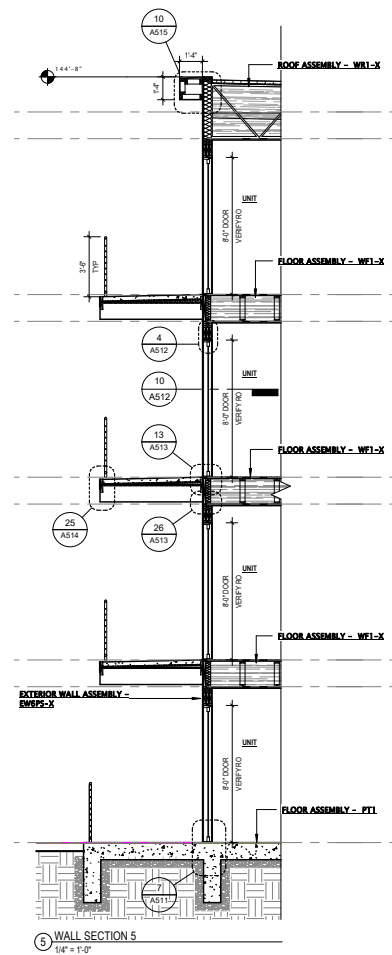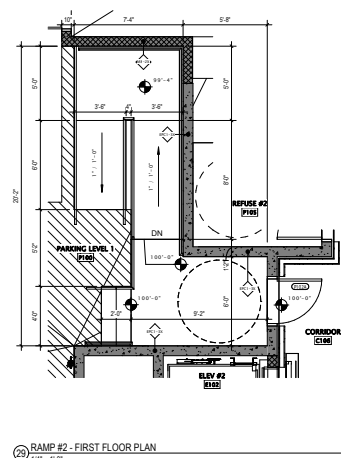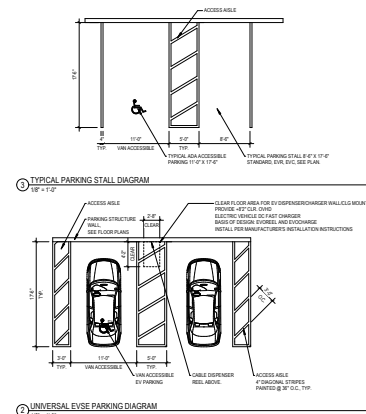


Shown are contributions alongside the broader project team, incorporating redlines and design updates across floor plans, enlarged plans, reflected ceiling plans, elevations, and sections. Work spanned schematic design through construction documents, including coordination with consultants on accessibility and building envelope compliance.


Type: Multifamily
Location: 8399 E 23rd, Denver, CO
Completion Date: Spring 2028
Client: Clear Sky Capital
Units: 259
Construction Cost: \$63 million
Programs: Revit, AutoCAD

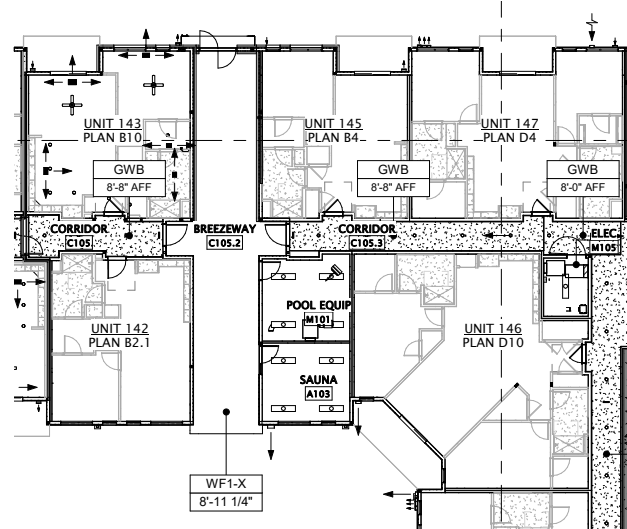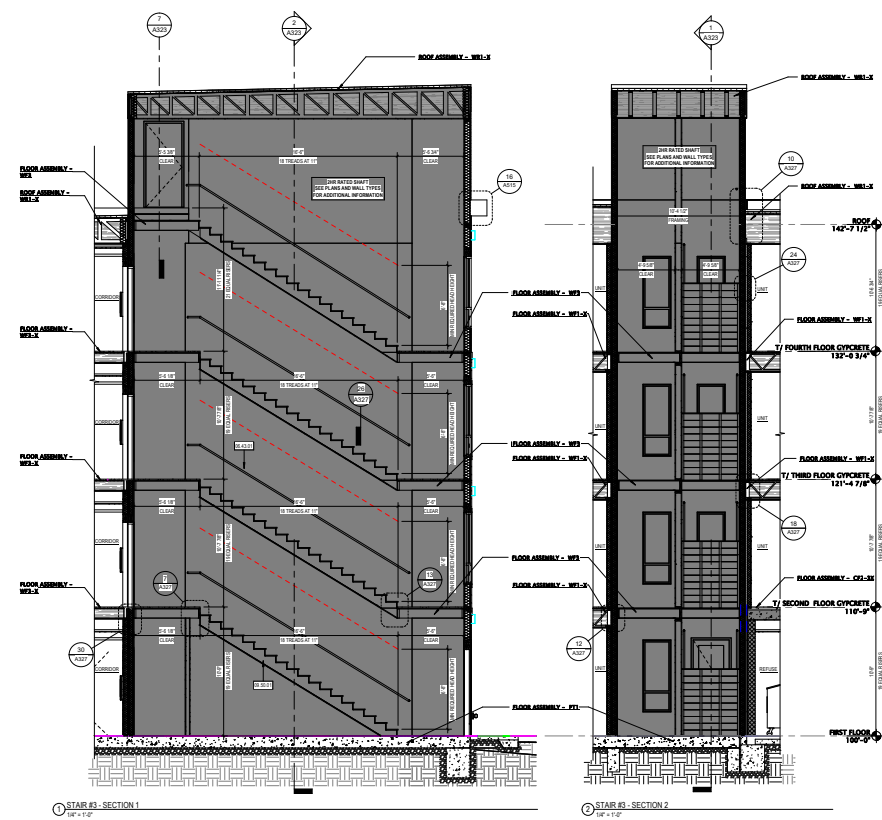

03 | RAVENFIELD

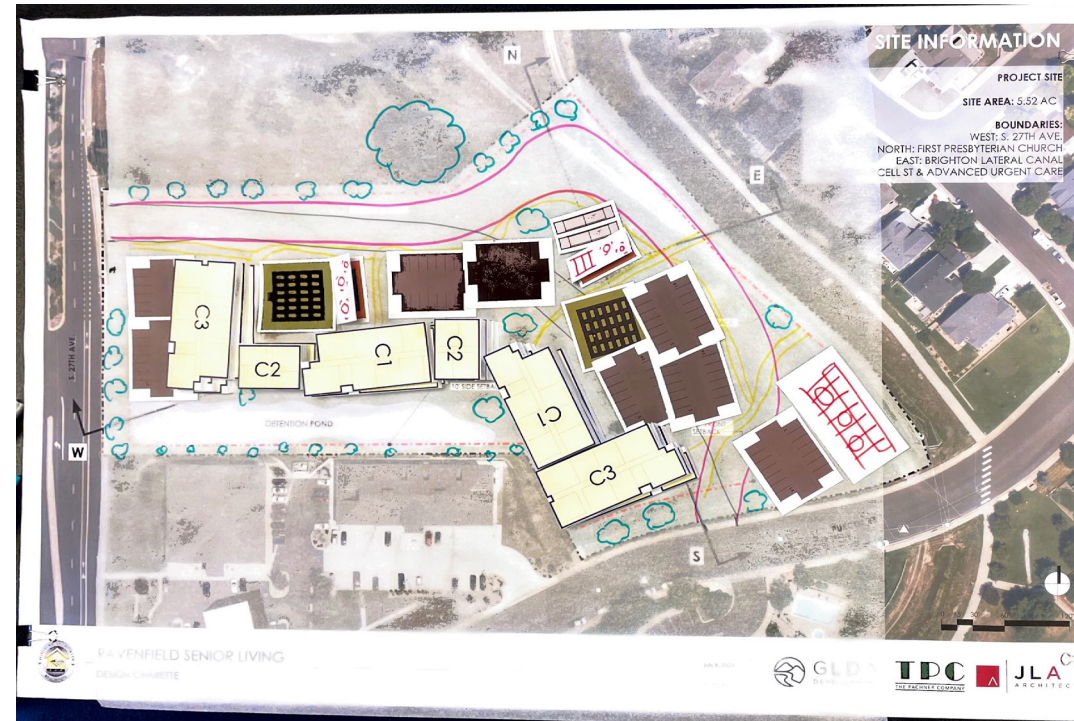


Type: Affordable Housing for Seniors
Location: 590 S 27th Ave, Brighton, CO
Construction Start: May 2026
Client: Brighton Housing Authority
Units: 46

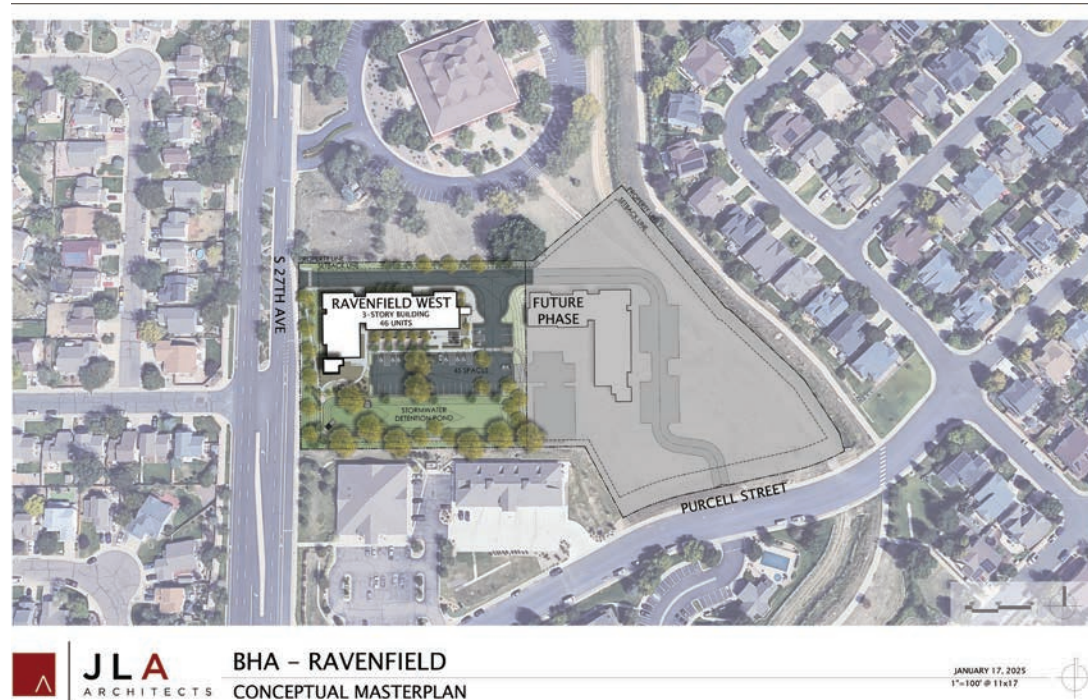


A 3-story, 46-unit LIHTC senior housing project by JLA Architects in Brighton, CO. Contributed during schematic design, participating in client meetings and a community design charrette with neighboring residents. Used scaled site elements to gather feedback, which informed the project's site organization and design.

04 | MASTER PLANS

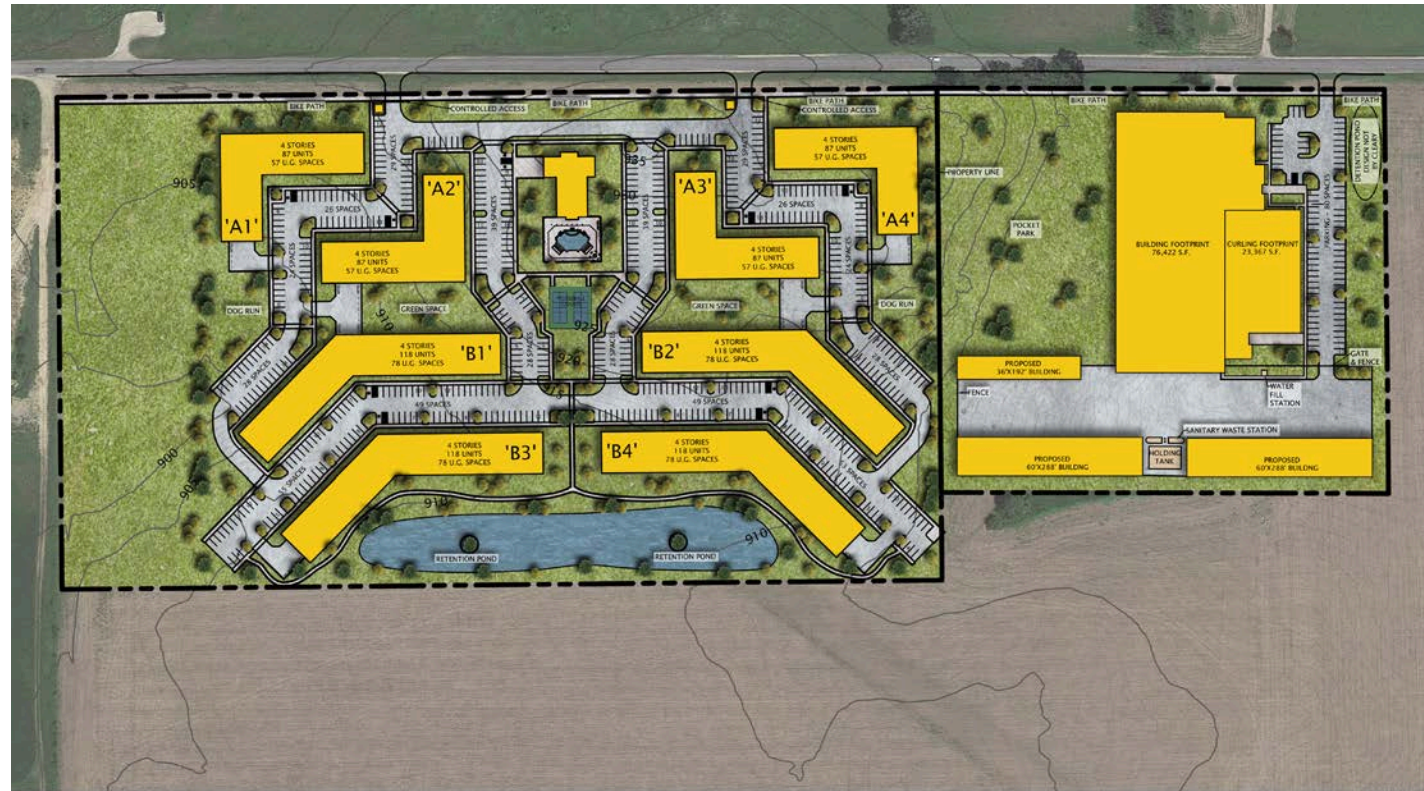

JLA ARCHITECTS BISHOP'S BAY APARTMENTS & WHEELHOUSE TENNIS CENTER JUNE 2, 2023
 RENDERED MASTERPLAN 1"=130' @ 11x17
T.Wall Enterprises LLC Creating Places Where People Interact

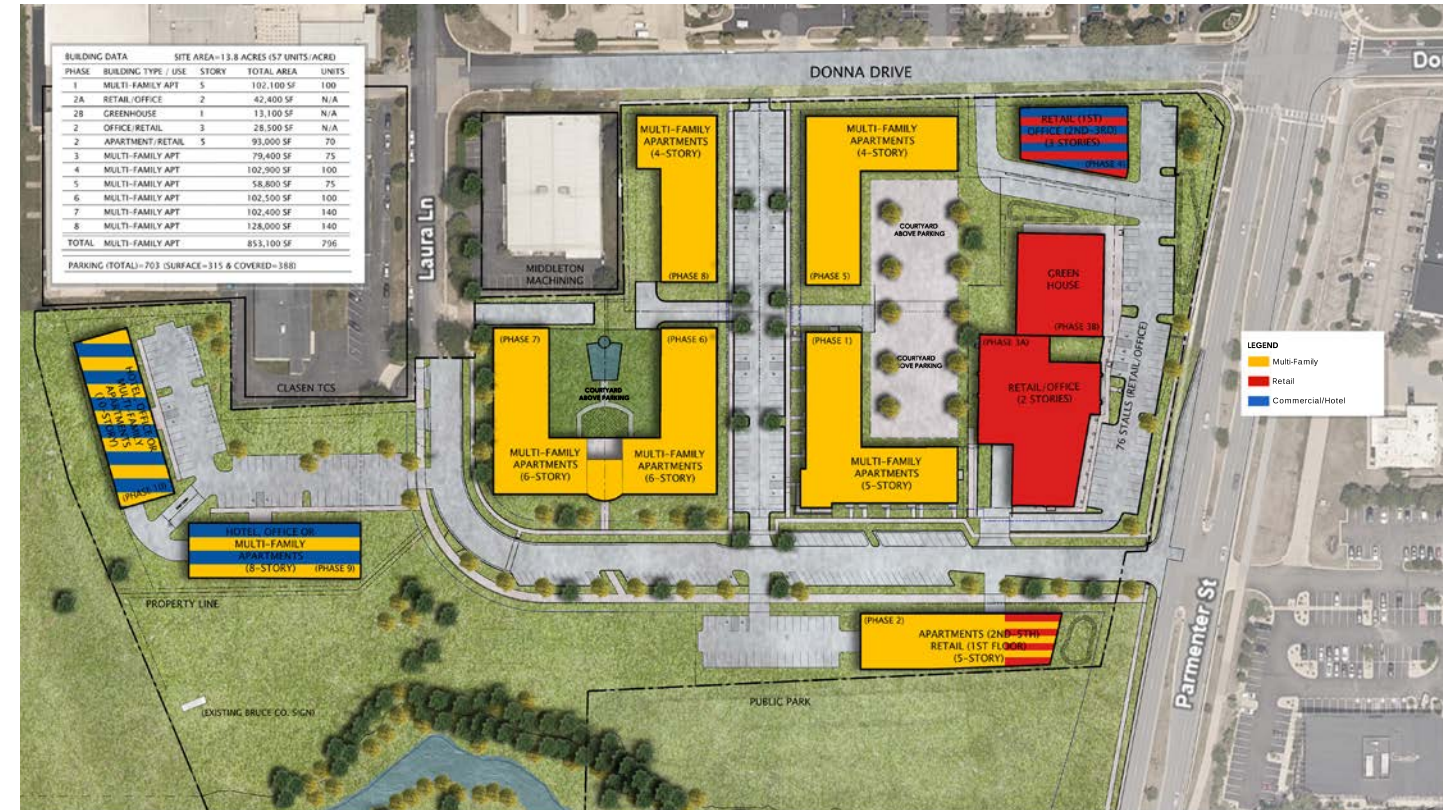


JLA ARCHITECTS Garden District Masterplan
 Conceptual Masterplan December 18, 2025
T.Wall Enterprises LLC Development, LLC

Two adjacent developments for returning client T Wall Enterprises in Wisconsin. Bishop's Bay Apartments is an approximately 820-unit multifamily development with 8 4-story residential buildings, underground and site parking, and several amenities. The adjacent Wheelhouse Tennis Center includes a 76,422 SF primary facility and curling hall. Involvement focused on master planning; subsequent project phases are not shown.

Types: Multifamily, Mixed-Use
Location: Wisconsin
Client: T Wall Enterprises
Bishop's Bay: 820 Units
Garden District: 796 Units
Programs: AutoCAD, Photoshop


A mixed-use master plan for returning client T Wall Enterprises in Wisconsin, totaling nearly 1,000,000 SF. The plan includes residential, hospitality, office, retail, and community buildings ranging from 3 to 10 stories. Involvement focused on master planning; subsequent project phases are not shown.

05 | MUSEUM OF NATIVE AMERICAN ART

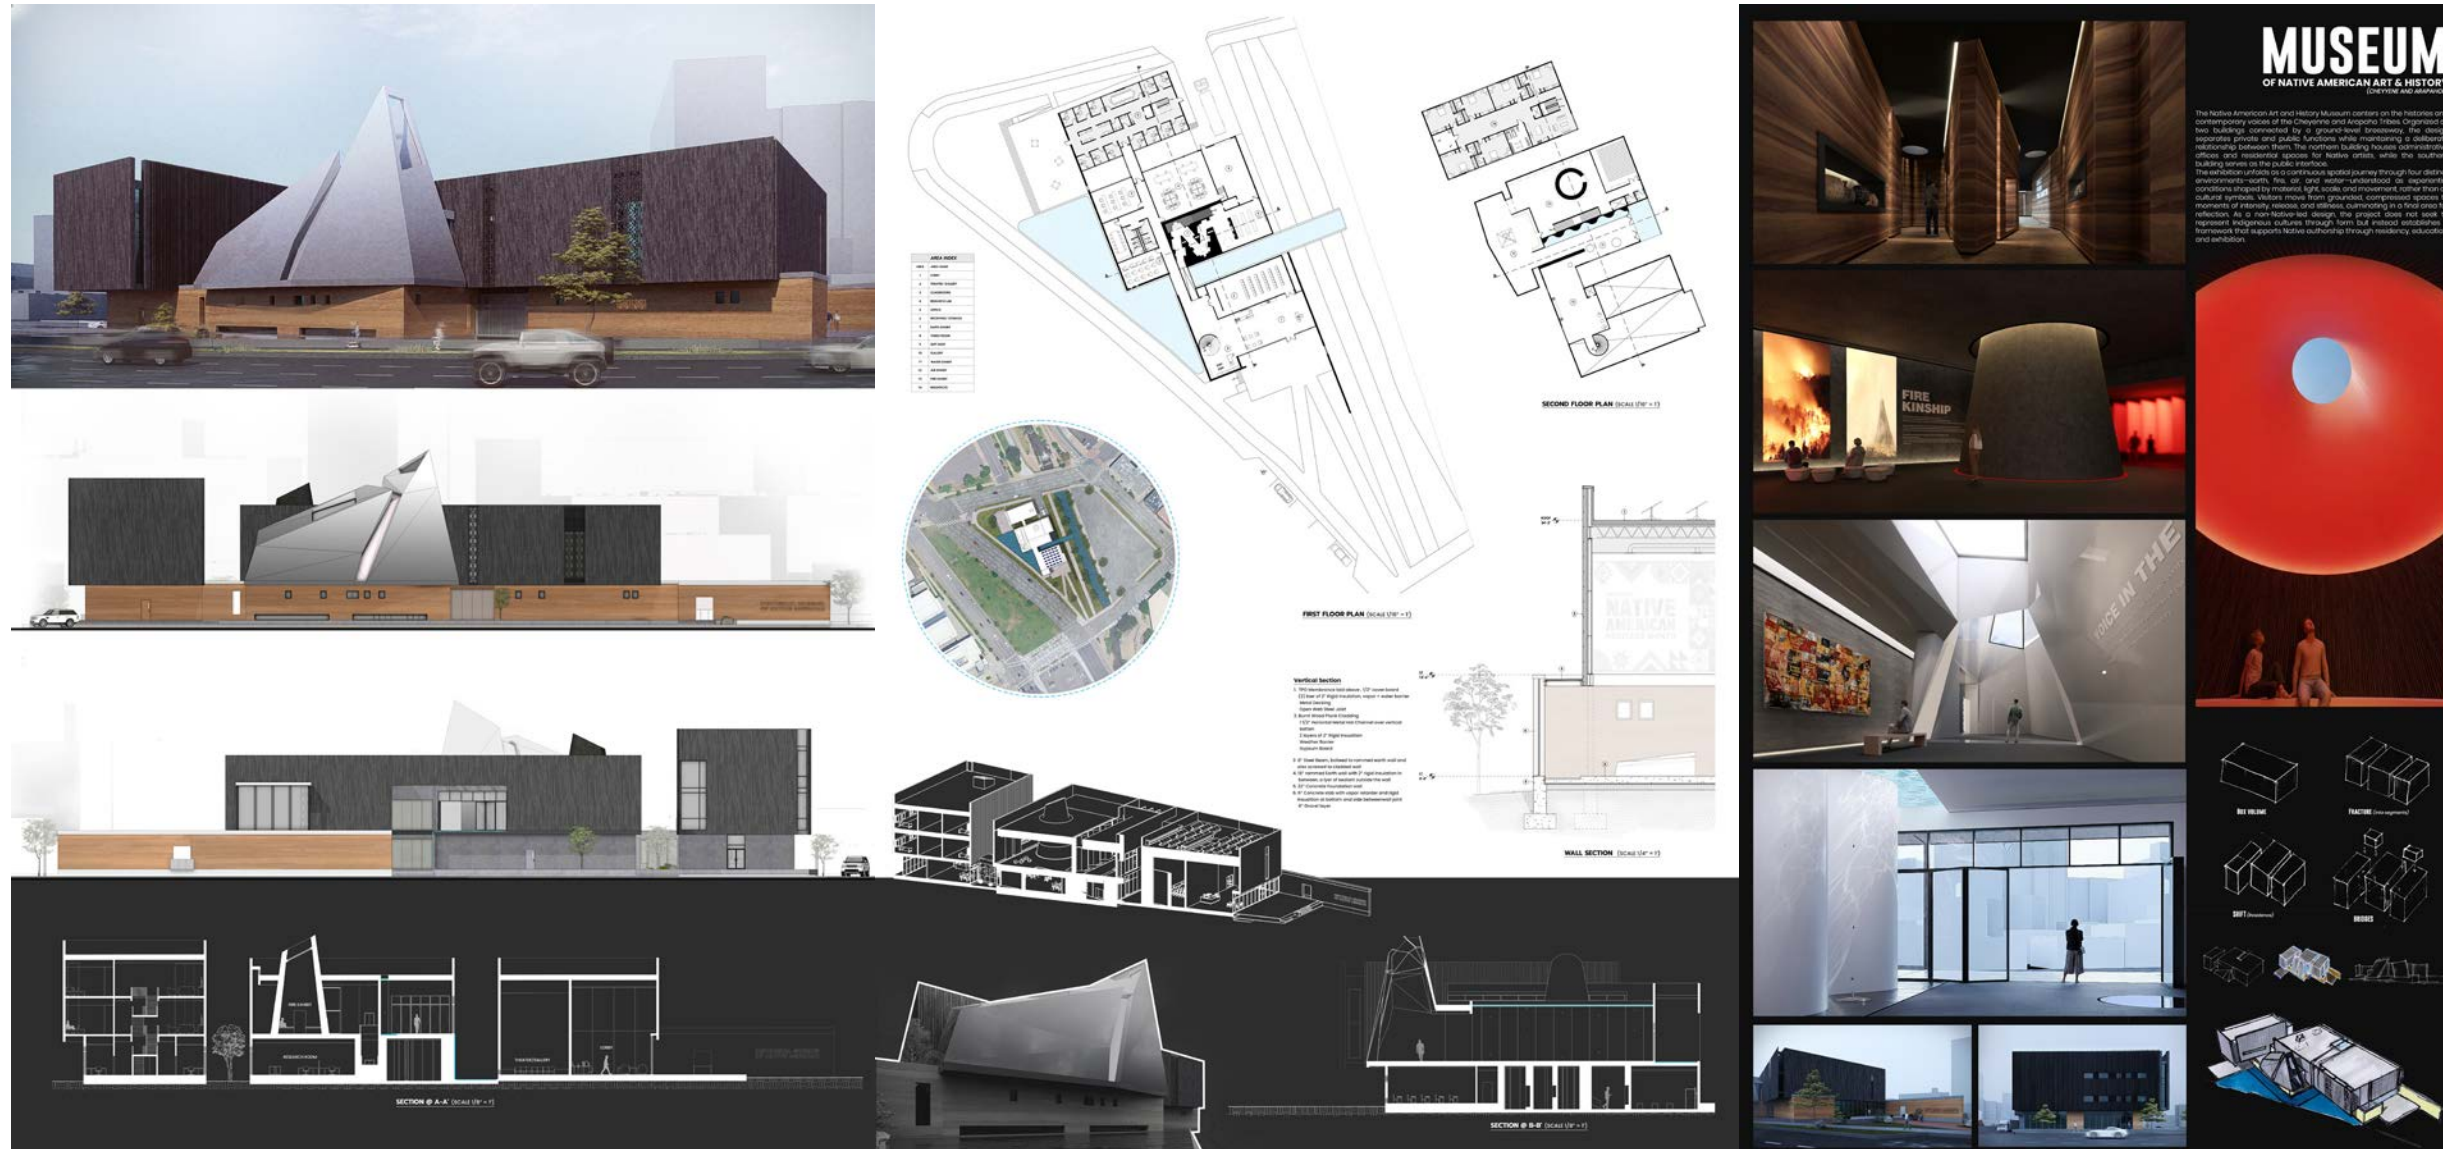


A museum honoring the histories and contemporary voices of the Cheyenne and Arapaho tribes, organized as two buildings connected by a ground-level breezeway. The south building houses the main museum, where visitors move through four exhibit spaces - earth, fire, sky, and water - each defined by distinct material, light, and sensory conditions. The north building contains offices, classrooms, and artist-in-residence housing for Indigenous artists. The design establishes a framework for native authorship through residency, education, and exhibition.

06 | MODEST MONUMENTALITY

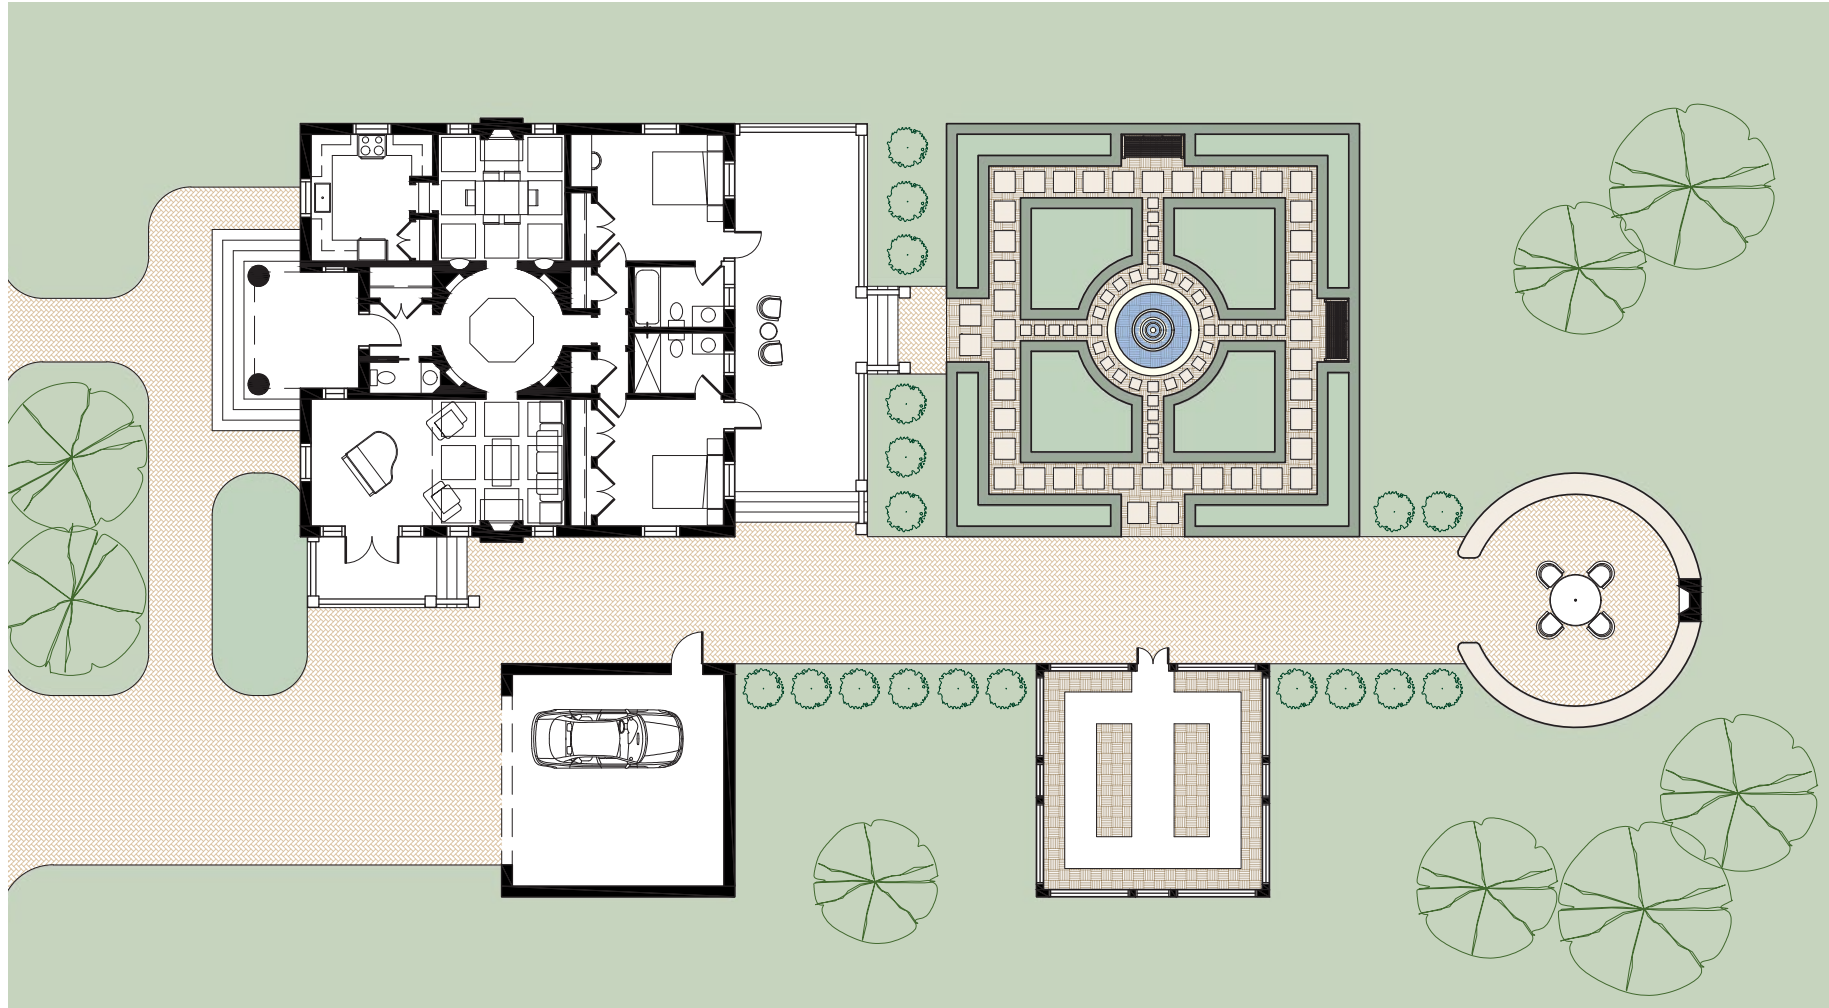

Type: Residential
Location: Morrison, CO
Studio: Grad Studio IV
Area: 1,543 SF
Site: 0.40 Acres
Programs: AutoCAD, Revit,
Twinmotion, Photoshop

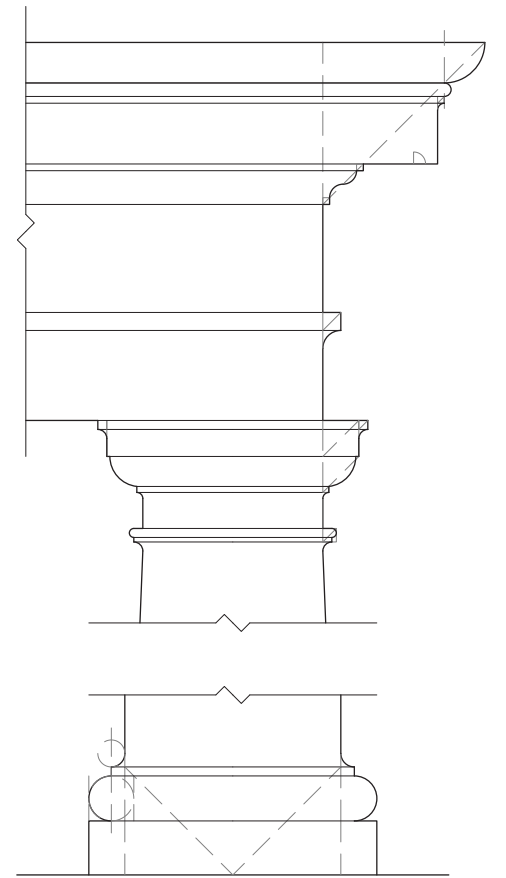



A small single-family residence informed by classical architectural principles of symmetry, procession, and proportion. The plan centers on a rotunda capped by a cupola and widow's walk. The dining and kitchen occupy one wing, a large great room in the other, while the rear wing contains a primary suite and a guest/children's bedroom.



07 | TECHNICAL SKETCHING


MCA

MIRANDA MORTON

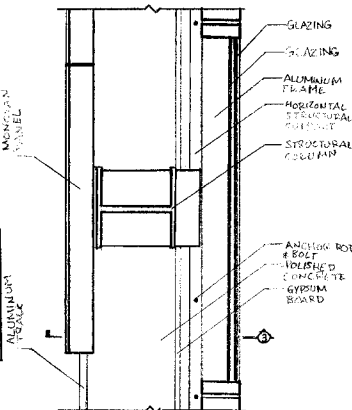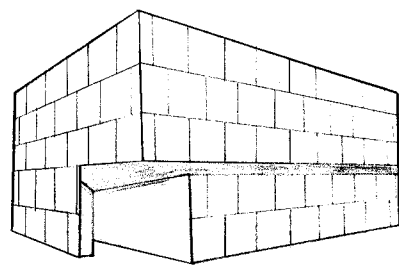

1 PERSPECTIVE
NOT TO SCALE



2 ENLARGED FLOOR PLAN
1" = 1'-0"

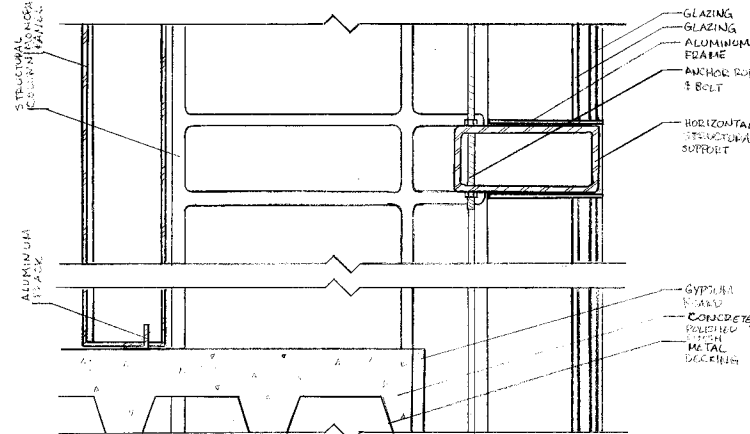

3 SECTION DETAIL
3" = 1'-0"


CSM

MIRANDA MORTON

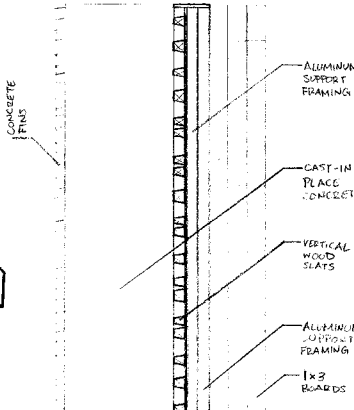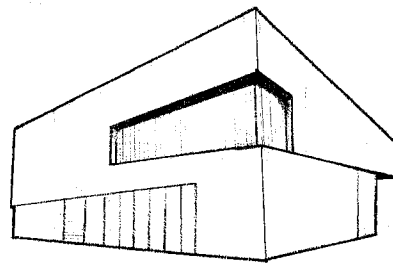

1 PERSPECTIVE
NOT TO SCALE



2 ENLARGED FLOOR PLAN
3/4" = 1'-0"

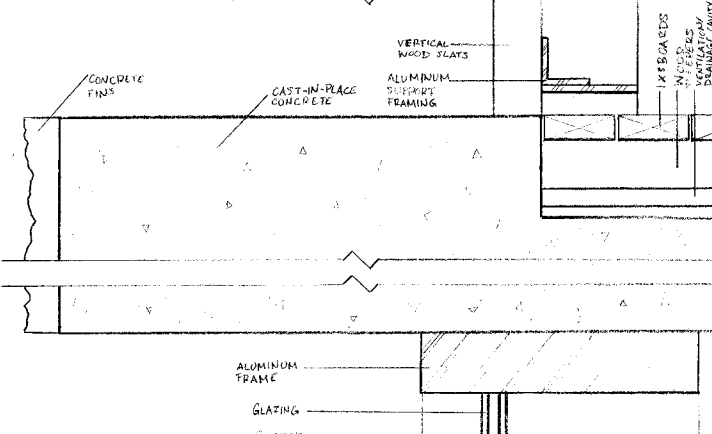

3 SECTION DETAIL
3" = 1'-0"


Populus

MIRANDA MORTON

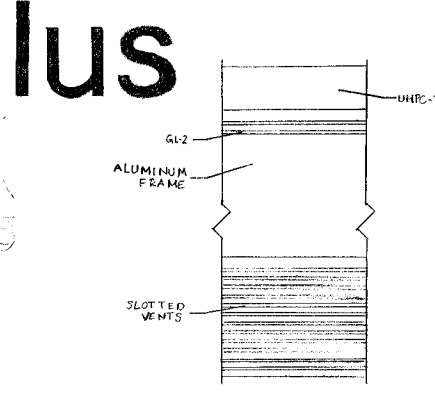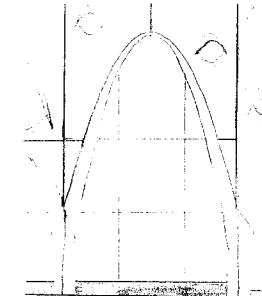

1 PERSPECTIVE
NOT TO SCALE


2 ENLARGED FLOOR PLAN
3/4" = 1'-0"

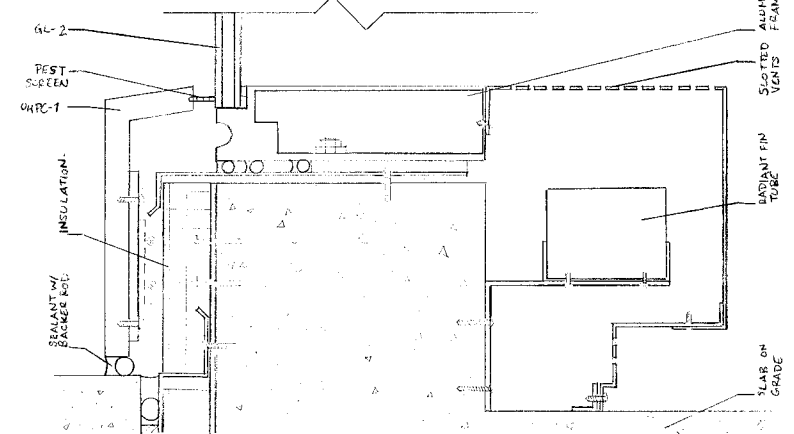

3 SECTION DETAIL
3" = 1'-0"

A series of hand-drawn studies analyzing three contemporary Denver Buildings: the Museum of Contemporary Art, the Clyfford Still Museum, and the Populus Hotel. Each study includes a perspective, an enlarged floor plan, and a section detail, all drafted by hand and to scale on 8.5" x 11" paper.

08 | COMMONS PARK

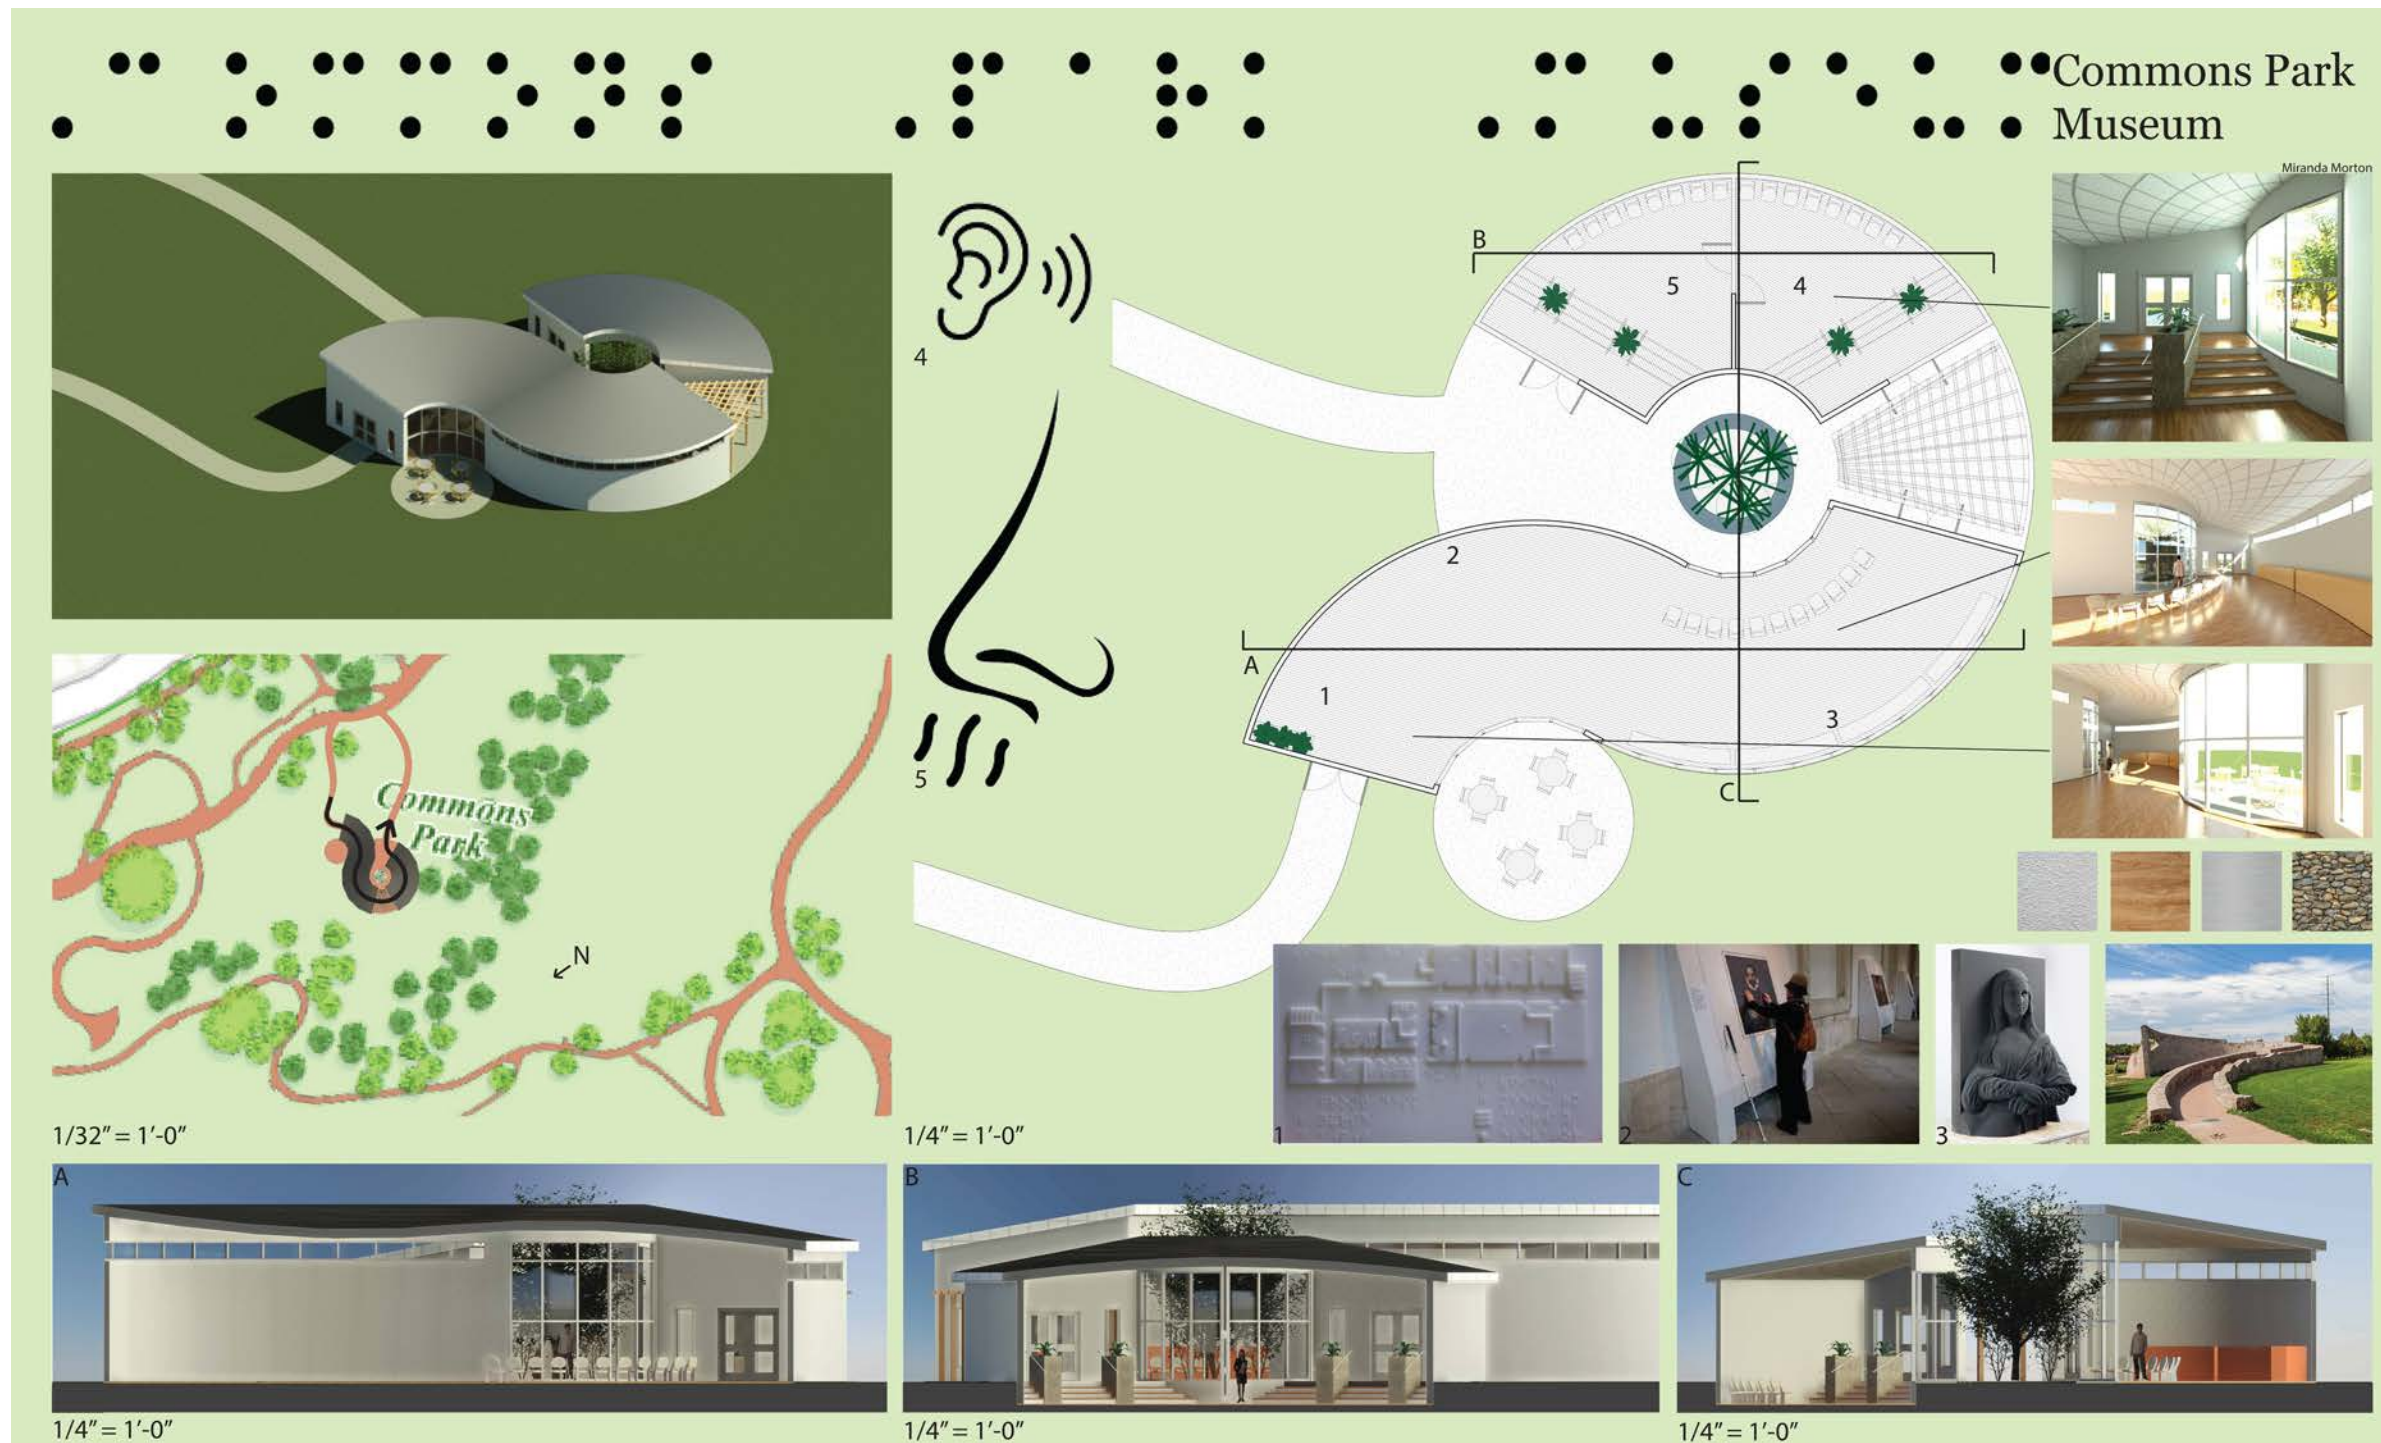

Commons Park
Museum

Type: Museum
Location: Denver, CO
Studio: Undergrad Studio II
Area: 2,300 SF
Programs: Revit, InDesign

A museum in Commons Park, Denver, created for visitors who are blind or visually impaired. The S-shaped building contains tactile 3D artwork, while the C-shaped building houses audio- and scent-based exhibits.